

Daftar kotak inbow — stop kontak & saklar Panasonic

Rumah Mbak Alfi · revisi 08-10-2026 · 1 kotak = 1 stop kontak / 1 saklar / 2 saklar · ID sama dengan label di model 3D (tekan E) dan angka di denah listrik 2D. Posisi x dari batas kavling kiri, z dari batas belakang (rumah x 3–10, z 3,5–13,5); h = tinggi as kotak dari lantai. Merah = tambahan / perubahan dari DED.

Lantai 1 — 32 kotak (23 stop kontak, 3 × 1 saklar, 5 × 2 saklar)

ID	Ruang	Isi kotak	h (m)	x, z (m)	Tembok	Keterangan
1-01	Teras belakang	1 stop kontak	1.20	9.88, 2.62	kanan	teras belakang: mesin cuci (di atas mesin, h 1,2)
1-02	Teras belakang	1 stop kontak	1.20	9.88, 3.27	kanan	REVISI: teras belakang: pompa pendorong (di atas pompa, h 1,2; DED: z 2.77 → digeser 50 cm)
1-03	Dapur	1 stop kontak	1.15	3.78, 3.56	belakang	BARU: dapur, tembok belakang di pojok kiri atas meja (rice cooker/microwave), jauh dari sink
1-04	Dapur	1 stop kontak	1.15	4.00, 3.56	belakang	BARU: dapur, tembok belakang di pojok kiri atas meja
1-05	Dapur	1 stop kontak	0.40	6.10, 3.58	belakang	dapur, tembok belakang (kulkas)
1-06	Dapur	1 stop kontak	0.40	6.30, 3.58	belakang	dapur, tembok belakang (kulkas)
1-07	Dapur	1 stop kontak	1.15	3.07, 5.25	kiri	dapur, di atas meja dapur, kanan jendela (gambar: z 5.47/5.69 menumpuk kusen jendela z 5.6–6.6 → digeser 22 cm)
1-08	Dapur	1 stop kontak	1.15	3.07, 5.47	kiri	dapur, di atas meja dapur
1-09	R. makan	1 stop kontak	0.40	5.56, 6.94	depan	ruang makan, tembok toilet
1-10	R. makan	1 stop kontak	0.40	5.77, 6.94	depan	ruang makan, tembok toilet
1-11	R. makan	2 saklar	1.40	6.30, 6.94	depan	ruang makan, tembok toilet → lampu dapur, r. makan, lorong
1-12	Pintu belakang (r. makan)	2 saklar	1.40	7.70, 3.56	belakang	REVISI: saklar ganda di kanan pintu belakang → lampu teras belakang + area jemur (DED: ganda; kotak Panasonic 2 saklar)
1-13	Pintu belakang (r. makan)	1 saklar tukar	1.40	7.80, 3.56	belakang	BARU: saklar tukar (two-way) lampu tangga/void, kotak kedua di kanan saklar ganda pintu belakang
1-14	Lemari bawah tangga	1 stop kontak (NVR/router)	0.40	9.88, 8.35	kanan	BARU: stop kontak NVR 4 ch PoE, di dalam lemari bawah tangga (bagian tinggi dekat r. keluarga)
1-15	Lemari bawah tangga	1 stop kontak (NVR/router)	0.40	9.88, 8.45	kanan	BARU: stop kontak router/switch, kotak kedua di samping stop kontak NVR
1-16	Toilet	1 stop kontak water heater (IP44)	1.82	4.45, 7.09	belakang	BARU: stop kontak water heater toilet lt1 (IP44), tembok sisi r. makan, kanan unit; 1,9 m di atas lantai toilet (–0,03)
1-17	Lorong	1 saklar	1.40	5.42, 8.44	depan	lorong depan toilet → lampu toilet
1-18	KT1	1 stop kontak	0.40	4.99, 8.56	belakang	KT1, tembok belakang (kiri pintu)
1-19	KT1	1 saklar	1.40	5.42, 8.56	belakang	KT1, kiri pintu → lampu KT1
1-20	KT1	1 stop kontak AC	2.40	3.06, 8.75	kiri	BARU: stop kontak AC KT1, tembok kiri mepet pojok tembok belakang (17 cm), di kiri unit indoor yang di atas jendela
1-21	KT1	1 stop kontak	0.40	3.06, 10.22	kiri	KT1, tembok kiri
1-22	R. keluarga	1 stop kontak	0.40	9.87, 9.20	kanan	REVISI: R. keluarga, tembok kanan dekat lemari bawah tangga, di balik pohon pot (DED: z 11.19)
1-23	R. keluarga	1 stop kontak	0.78	6.68, 10.30	kiri	BARU: dinding TV, di bawah TV di atas konsol, kotak 1 dari 4 (TV)
1-24	R. keluarga	1 stop kontak	0.78	6.68, 10.52	kiri	BARU: dinding TV, kotak 2 dari 4 (set-top box / Android TV box)
1-25	R. keluarga	1 stop kontak	0.78	6.68, 10.74	kiri	BARU: dinding TV, kotak 3 dari 4 (soundbar)
1-26	R. keluarga	1 stop kontak	0.78	6.68, 10.96	kiri	BARU: dinding TV, kotak 4 dari 4 (konsol game / router)
1-27	R. keluarga	1 stop kontak antena TV	0.78	6.68, 11.18	kiri	BARU: stop kontak antena TV (coax) di bawah TV, kotak ke-5 di kanan 4 stop kontak
1-28	R. keluarga	2 saklar	1.40	6.68, 11.69	kiri	R. keluarga, di muka panel TV → lampu r. keluarga
1-29	R. keluarga	2 saklar	1.40	6.66, 12.02	kiri	R. keluarga, samping pintu utama → lampu teras & carport
1-30	R. keluarga	1 stop kontak	0.35	9.87, 12.30	kanan	REVISI: R. keluarga, tembok kanan depan, di bawah meja samping melayang (bawah meja 0.41) (DED: z 10.72 di belakang sofa → digeser supaya sofa bisa mepet)

ID	Ruang	Isi kotak	h (m)	x, z (m)	Tembok	Keterangan
1-31	R. keluarga	1 stop kontak	0.35	9.87, 12.52	kanan	REVISI: R. keluarga, tembok kanan depan, di balik meja samping (DED: z 10.94)
1-32	Selasar samping (luar)	2 saklar	1.40	2.94, 10.22	kanan	teras samping (luar) → lampu taman/pagar

Lantai 2 — 23 kotak (14 stop kontak, 4 × 1 saklar, 4 × 2 saklar)


ID	Ruang	Isi kotak	h (m)	x, z (m)	Tembok	Keterangan
2-01	KT2	1 stop kontak	0.40	3.06, 5.33	kiri	KT2, tembok kiri
2-02	KT2	1 stop kontak AC	2.40	3.06, 5.45	kiri	BARU: stop kontak AC KT2, tembok kiri di kiri unit indoor yang di atas jendela
2-03	KT2	1 stop kontak	0.40	6.43, 5.45	kanan	KT2, tembok kanan
2-04	KT2	1 saklar	1.40	6.43, 5.88	kanan	KT2, samping pintu → lampu KT2 (simbol DED: tunggal, 1 kelompok lampu)
2-05	Selasar	1 saklar	1.40	7.73, 3.56	belakang	selasar, kanan pintu balkon belakang → lampu balkon
2-06	Selasar	1 stop kontak	0.40	6.56, 5.45	kiri	selasar, tembok KT2
2-07	Selasar	2 saklar	1.40	6.56, 8.15	kiri	REVISI: selasar, samping pintu toilet kanan → 1 tuts lampu toilet kanan + 1 tuts 3 lampu selasar (2 selasar + 1 depan pintu KTU); menggantikan saklar selasar DED di z 5,88
2-08	Toilet kiri (KTU)	1 stop kontak water heater (IP44)	1.90	4.50, 7.09	belakang	BARU: stop kontak water heater toilet lt2 kiri (di dalam KTU, IP44), tembok sisi KT2, kanan unit, 1,1 m dari kepala shower
2-09	KT utama	2 saklar	1.40	4.07, 8.56	belakang	KTU, kanan pintu toilet → lampu toilet kiri + lampu balkon samping kiri (simbol DED: ganda, 2 kelompok)
2-10	KT utama	1 saklar	1.40	6.43, 9.57	kanan	KTU, samping pintu → lampu KTU
2-11	KT utama	1 stop kontak	0.40	6.43, 10.01	kanan	KTU, tembok kanan (meja rias)
2-12	KT utama	1 stop kontak AC	2.40	3.06, 10.30	kiri	BARU: stop kontak AC KTU, tembok kiri di kanan unit indoor yang di atas pintu geser balkon
2-13	KT utama	1 stop kontak	0.40	3.06, 10.75	kiri	KTU, tembok kiri
2-14	R. keluarga lt2	1 saklar tukar	1.40	9.88, 9.45	kanan	BARU: saklar tukar (two-way) lampu tangga/void di tembok luar, tepat setelah anak tangga teratas — pasangan saklar triple lt1 di pintu belakang
2-15	R. keluarga lt2	2 saklar	1.40	9.88, 9.55	kanan	REVISI: R. keluarga lt2, tembok luar setelah tangga, kotak di samping saklar tukar → lampu r. keluarga lt2 (DED: di tembok KTU samping pintu)
2-16	R. keluarga lt2	1 stop kontak	0.40	6.56, 9.72	kiri	BARU: R. keluarga lt2, tembok KTU (seberang), strip bebas di kanan pintu KTU
2-17	R. keluarga lt2	1 stop kontak	1.05	6.56, 10.90	kiri	BARU: R. keluarga lt2, tembok KTU di atas sideboard (top 0.80)
2-18	R. keluarga lt2	1 stop kontak	1.05	6.56, 11.12	kiri	BARU: R. keluarga lt2, tembok KTU di atas sideboard
2-19	R. keluarga lt2	2 saklar	1.40	6.56, 12.02	kiri	R. keluarga lt2, samping pintu balkon → lampu balkon depan + sorot
2-20	R. keluarga lt2	1 stop kontak antena TV	0.40	9.88, 12.19	kanan	BARU: stop kontak antena TV (coax) di bawah meja kerja, kiri 3 stop kontak meja
2-21	R. keluarga lt2	1 stop kontak	0.40	9.88, 12.41	kanan	R. keluarga lt2, tembok kanan depan
2-22	R. keluarga lt2	1 stop kontak	0.40	9.88, 12.63	kanan	R. keluarga lt2, tembok kanan depan

ID	Ruang	Isi kotak	h (m)	x, z (m)	Tembok	Keterangan
2-23	R. keluarga lt2	1 stop kontak	0.40	9.88, 12.85	kanan	R. keluarga lt2, tembok kanan depan

Rekap belanja kotak

Kotak 1 stop kontak (termasuk 3 AC, 2 water heater IP44, 2 NVR)	37
Kotak 1 saklar (termasuk 2 saklar tukar)	7
Kotak 2 saklar	9
Kotak stop kontak antena TV (coax; 1 antena di atap + splitter 2 way)	2
Total kotak / inbow doos	55

Stop kontak water heater (1-16, 2-08) perlu varian tertutup (IP44). Ukuran pelat 90 mm = asumsi dari inbow doos 86 mm; cocokkan dengan kemasan produk. Dibuat otomatis dari data model 3D (scripts/denah-listrik.mjs).

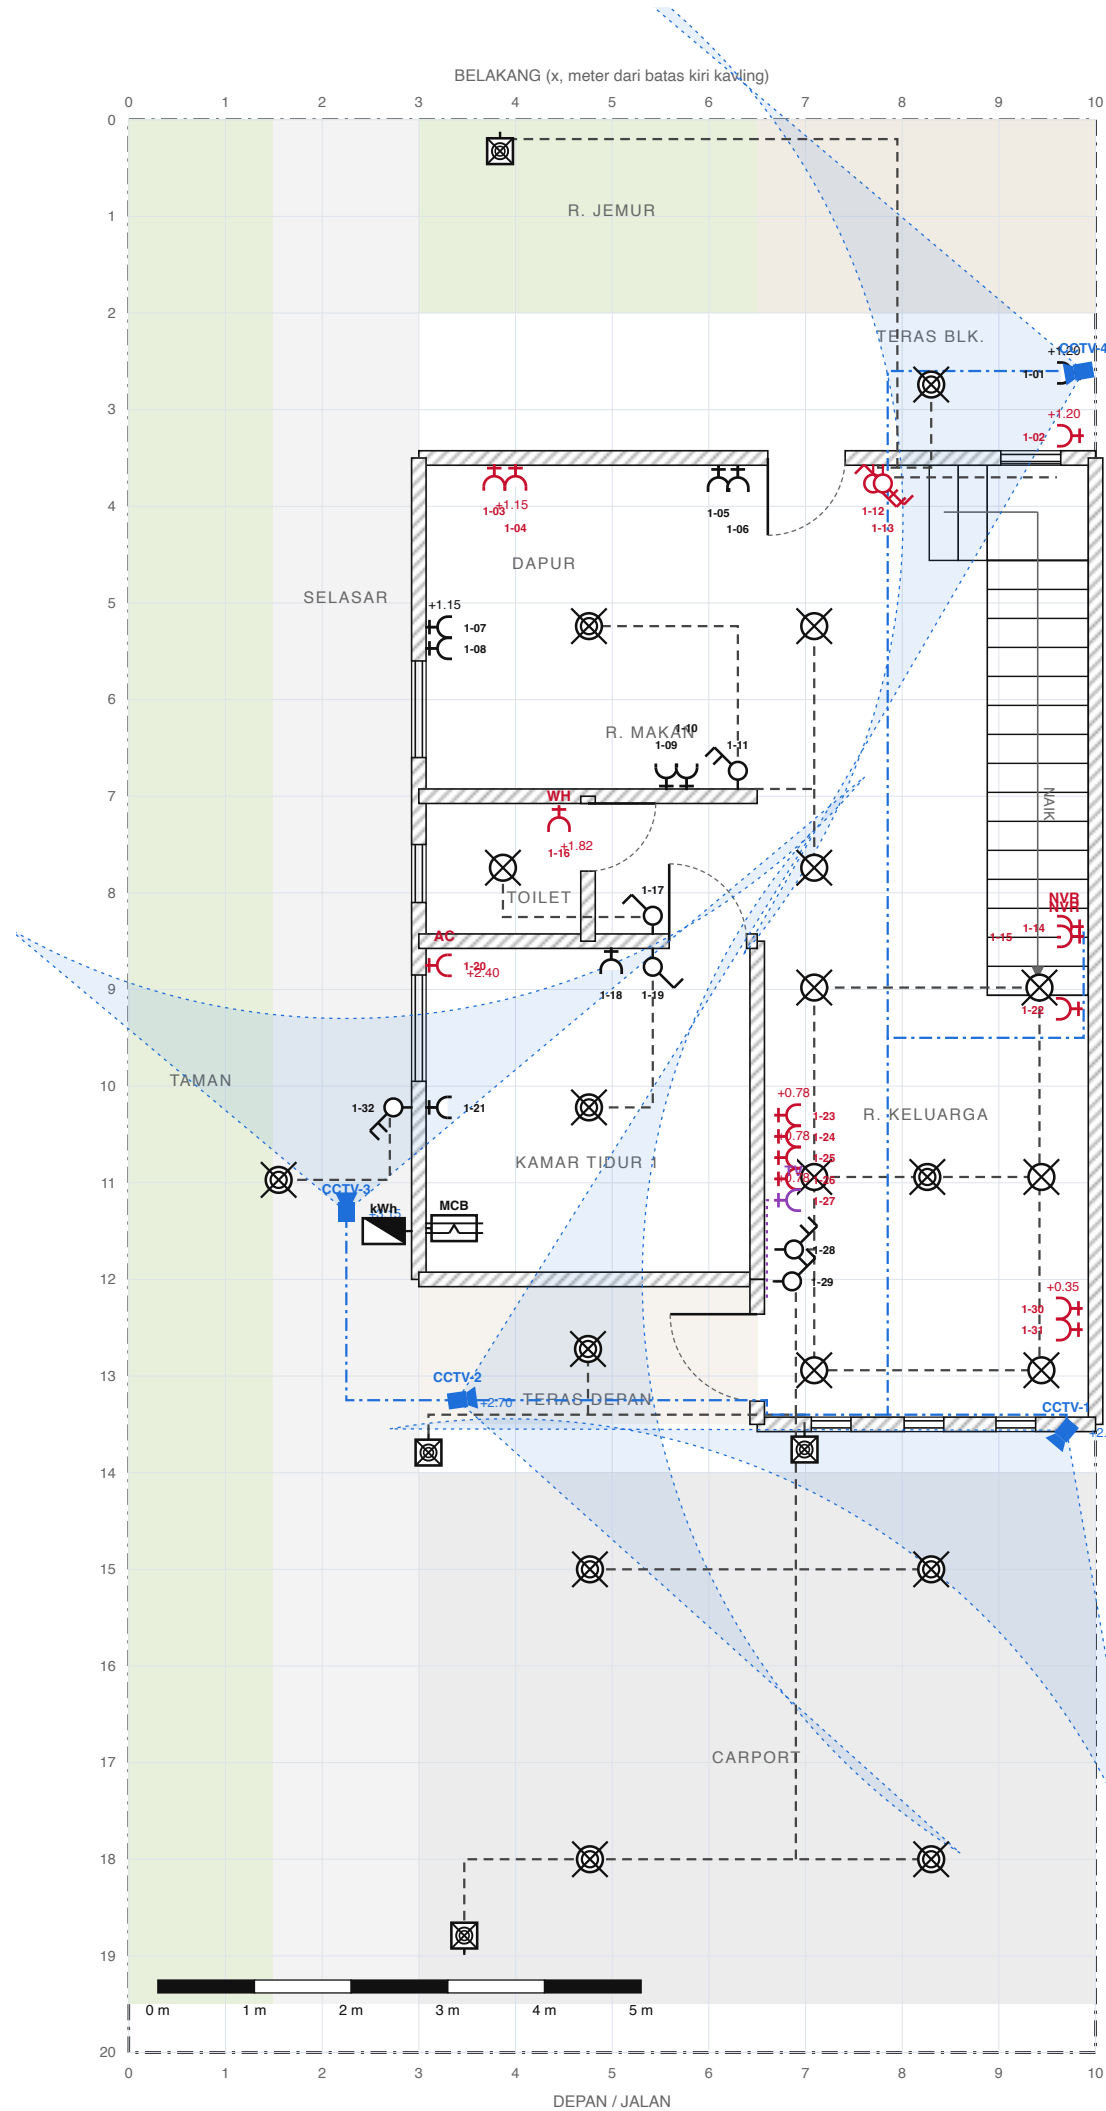

DENAH INSTALASI LISTRIK

LANTAI 1 — REVISI 08-10-2026

Rumah Mbak Alfi · skala 1 : 100 pada A3 (1 m = 60 px) · dasar: DED lembar 26 (hal. 69)


SIMBOL	KETERANGAN	ADA	BARU
	Stop kontak 1 ph 10/16 A, h 40 cm (dapur 115, mesin cuci 120)	13	+8
	Stop kontak AC, h 240 cm (unit indoor di atas jendela)	0	+1
	Stop kontak water heater IP44, h 190 cm, grup sendiri	0	+1
	Stop kontak antenna TV (coax IEC), 1 antenna di atap + splitter 2 way	0	+1
	Saklar tunggal, h 140 cm	2	-
	Saklar ganda, h 140 cm	5	-
	Saklar tukar (two-way) lampu tangga, h 140 cm	0	+1
	Kotak inbow Panasonic (1 kotak = 1 stop kontak / 1 saklar / 2 saklar); angka = ID kotak (32 kotak, lihat daftar-kotak.md)		
	Lampu LED downlight 5 W	9	-
	Lampu LED downlight 9 W (termasuk 4 carport)	10	-
	Lampu LED sorot / dinding outdoor	4	-
	Box MCB 4 group x 10 A, h 175 cm	1	-
	kWh meter PLN 2200 VA (sisi luar), h 170 cm	1	-
	Jalur kabel NYM 2x2,5 mm² dalam pipa, di bawah dak/plafon		
	CCTV IP PoE 2 MP outdoor (kerucut = sudut pandang 100°, 7 m)	0	+4
	NVR 4 ch PoE + HDD di lemari bawah tangga (stop kontak ganda)	0	+2
	Kabel data CAT6 ke NVR, dalam pipa 3/4"		
	Kabel coax RG6 antenna (splitter di plafon r. keluarga lt2)		

REVISI 08-10-2026 (merah = tambahan / perubahan dari DED)

- teras belakang: pompa mendorong (di atas pompa, h 1,2; DED: z 2.77 → digeser 50 cm) (h 1.20 m)
- dapur, tembok belakang di pojok kiri atas meja (rice cooker/microwave), jauh dari sink (h 1.15 m)
- dapur, tembok belakang di pojok kiri atas meja (h 1.15 m)
- R. keluarga, tembok kanan depan, di bawah meja samping melayang (bawah meja 0.41) (DED: z 10.72 di belakang sofa → digeser supaya sofa bisa mepet) (h 0.35 m)
- R. keluarga, tembok kanan depan, di balik meja samping (DED: z 10.94) (h 0.35 m)
- R. keluarga, tembok kanan dekat lemari bawah tangga, di balik pohon pot (DED: z 11.19) (h 0.40 m)
- dinding TV: 4 stop kontak di bawah TV di atas konsol (TV, set-top box, soundbar, konsol/router) (h 0.78 m)
- stop kontak antenna TV (coax) di bawah TV, kotak ke-5 di kanan 4 stop kontak (h 0.78 m)
- stop kontak AC KT1, tembok kiri mepet pojok tembok belakang (17 cm), di kiri unit indoor yang di atas jendela (h 2.40 m)
- stop kontak water heater toilet lt1 (IP44), tembok sisi r. makan, kanan unit; 1,9 m di atas lantai toilet (−0.03) (h 1.82 m)
- CCTV-1 carport & gerbang: pojok kanan fasad di bawah tepi kanopi, menghadap gerbang (−40° ke kiri) sehingga mulut selasar kiri ikut terlihat, tunduk 15° (h 2.70 m)
- CCTV-2 teras depan & pintu utama: di plafon teras (bawah balkon) pojok kiri-depan, menghadap pintu utama (+x), tunduk 20° (h 2.70 m)
- CCTV-3 selasar samping kiri: di bawah balkon samping (tengah), menghadap ke belakang: selasar z 4–11 dalam 7 m, sambung dengan CCTV-4 yang menutup ujung belakang; mulut depan selasar ditangkap CCTV-1 (h 3.15 m)
- CCTV-4 belakang: tembok batas kanan di bawah balkon belakang, menghadap teras belakang, pintu belakang, area jemur & ujung belakang selasar (+10°), tunduk 17° (h 3.10 m)
- stop kontak NVR 4 ch PoE, di dalam lemari bawah tangga (bagian tinggi dekat r. keluarga) (h 0.40 m)
- stop kontak router/switch, kotak kedua di samping stop kontak NVR (h 0.40 m)
- saklar ganda di kanan pintu belakang → lampu teras belakang + area jemur (DED: ganda; kotak Panasonic 2 saklar) (h 1.40 m)
- saklar tukar (two-way) lampu tangga/void, kotak kedua di kanan saklar ganda pintu belakang (h 1.40 m)
- TV 65" diturunkan: bawah 0,80 m, tengah layar 1,22 m (mata duduk ±1,10 m)
- Stop kontak dapur kiri digeser 22 cm ke kanan jendela (jendela z 5,6–6,6)

CATATAN

Posisi simbol dari gambar DED 1:100 yang dikalibrasi ke tembok model 3D; titik dinding digambar di muka tembok. Tinggi pasang (dari lantai jadi) mengikuti praktik umum/PUIL karena DED tidak mencantumkan tinggi.
Angka +h.hh di samping simbol = tinggi yang menyimpang dari standar. Jalur kabel digambar skematis (ortogonal) mengikuti DED; kabel NYM dalam pipa PVC 5/8".
Rekomendasi: grup MCB dipisah (penerangan lt1/lt2, stop kontak lt1/lt2, AC lt1, AC lt2, water heater) → box 8 group, 7 MCB; 2200 VA cukup untuk ≤2 AC ½ PK + water heater tangkai low-watt, kalau 3 AC + pompa sebaiknya 3500 VA.

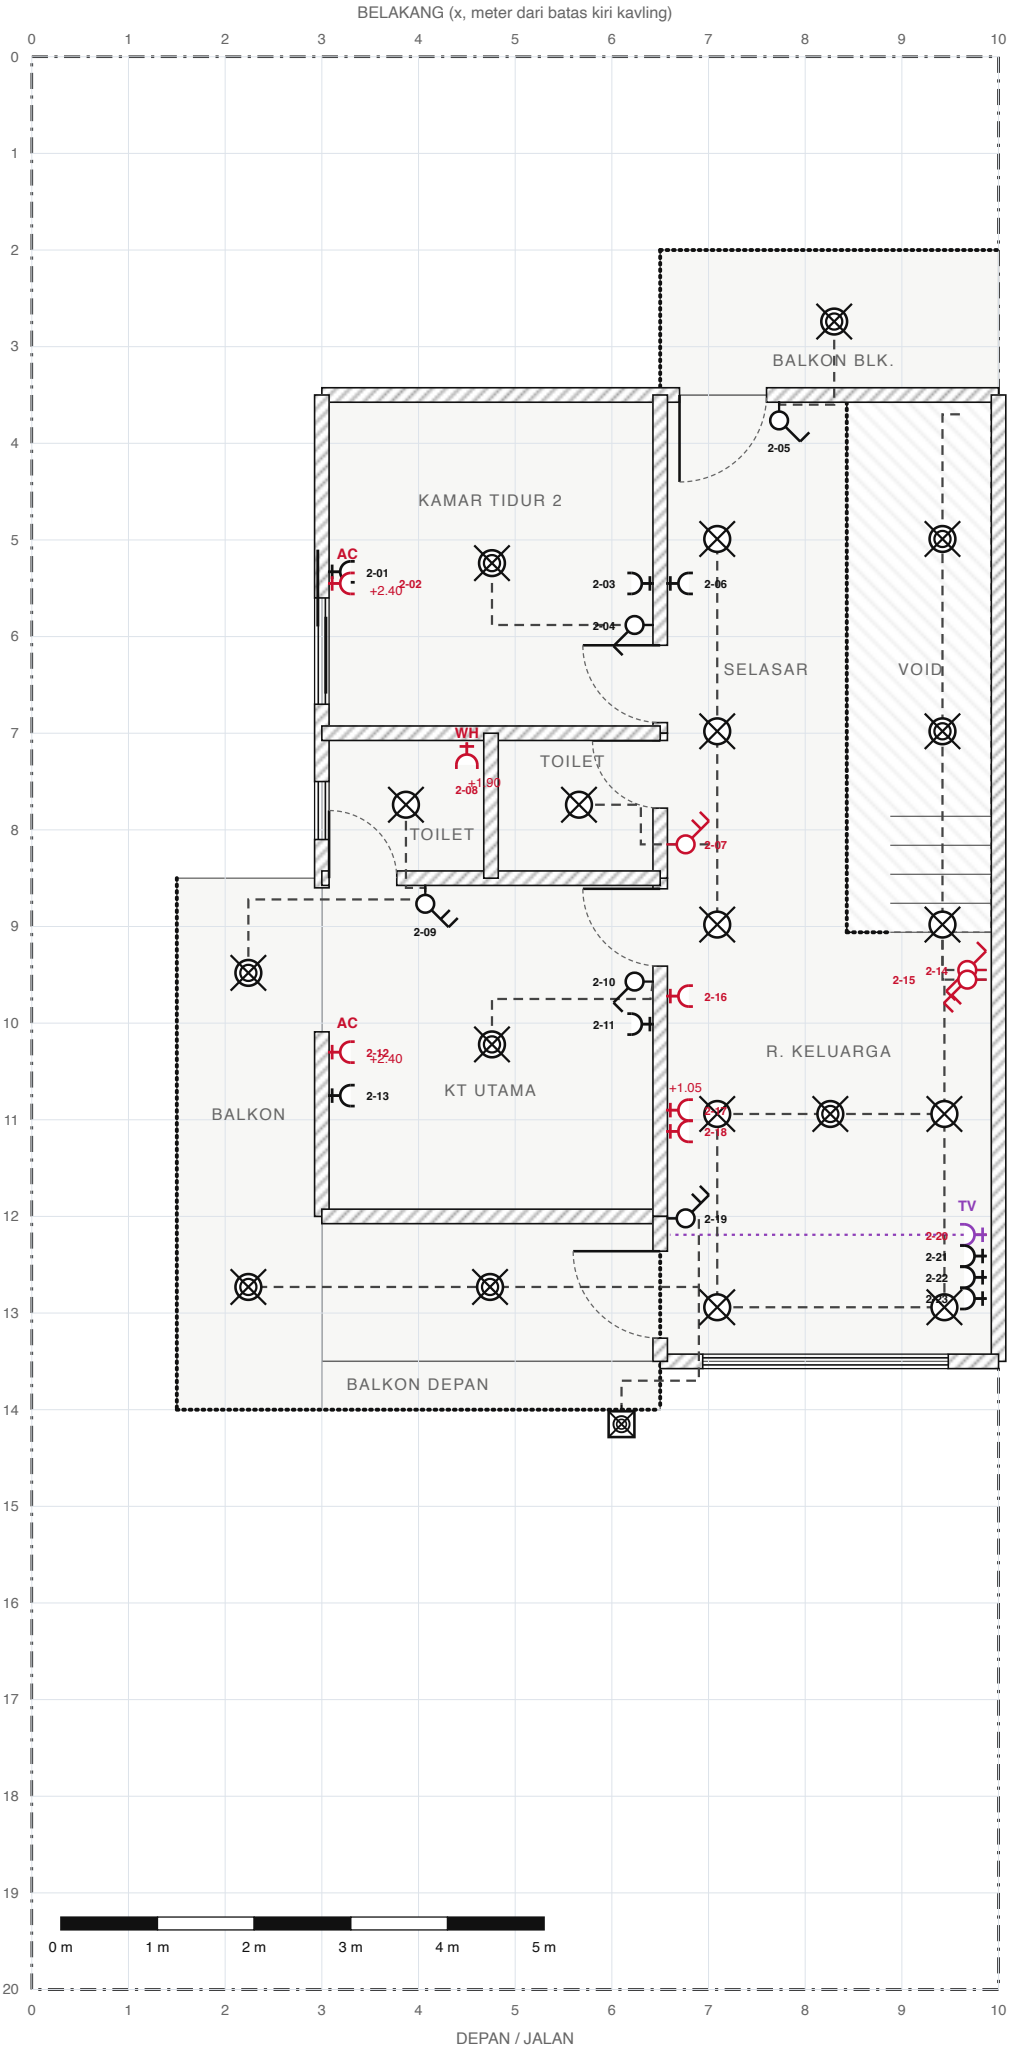

Dibuat otomatis dari data model 3D (scripts/denah-listrik.mjs) · 08-10-2026

DENAH INSTALASI LISTRIK

LANTAI 2 — REVISI 08-10-2026

Rumah Mbak Alfi · skala 1 : 100 pada A3 (1 m = 60 px) · dasar: DED lembar 27 (hal. 70)

SIMBOL	KETERANGAN	ADA	BARU
	Stop kontak 1 ph 10/16 A, h 40 cm (dapur 115, mesin cuci 120)	8	+3
	Stop kontak AC, h 240 cm (unit indoor di atas jendela)	0	+2
	Stop kontak water heater IP44, h 190 cm, grup sendiri	0	+1
	Stop kontak antenna TV (coax IEC), 1 antenna di atap + splitter 2 way	0	+1
	Saklar tunggal, h 140 cm	3	-
	Saklar ganda, h 140 cm	4	-
	Saklar tukar (two-way) lampu tangga, h 140 cm	0	+1
	Kotak inbow Panasonic (1 kotak = 1 stop kontak / 1 saklar / 2 saklar); angka = ID kotak (23 kotak, lihat daftar-kotak.md)		
	Lampu LED downlight 5 W	10	-
	Lampu LED downlight 9 W	9	-
	Lampu LED sorot / dinding outdoor	1	-
	Box MCB 4 group x 10 A, h 175 cm	0	-
	kWh meter PLN 2200 VA (sisi luar), h 170 cm	0	-
	Jalur kabel NYM 2x2,5 mm² dalam pipa, di bawah dak/plafon		
	Kabel coax RG6 antenna (splitter di plafon r. keluarga lt2)		

REVISI 08-10-2026 (merah = tambahan / perubahan dari DED)

- stop kontak antenna TV (coax) di bawah meja kerja, kiri 3 stop kontak meja (h 0.40 m)
- stop kontak AC KT2, tembok kiri di kiri unit indoor yang di atas jendela (h 2.40 m)
- stop kontak AC KTU, tembok kiri di kanan unit indoor yang di atas pintu geser balkon (h 2.40 m)
- R. keluarga lt2, tembok KTU (seberang), strip bebas di kanan pintu KTU (h 0.40 m)
- R. keluarga lt2, tembok KTU di atas sideboard (top 0.80) (h 1.05 m)
- R. keluarga lt2, tembok KTU di atas sideboard (h 1.05 m)
- stop kontak water heater toilet lt2 kiri (di dalam KTU, IP44), tembok sisi KT2, kanan unit, 1,1 m dari kepala shower (h 1.90 m)
- saklar tukar (two-way) lampu tangga/void di tembok luar, tepat setelah anak tangga teratas — pasangan saklar triple lt1 di pintu belakang (h 1.40 m)
- selasar, samping pintu toilet kanan → 1 tuts lampu toilet kanan + 1 tuts 3 lampu selasar (2 selasar + 1 depan pintu KTU); menggantikan saklar selasar DED di z 5.88 (h 1.40 m)
- R. keluarga lt2, tembok luar setelah tangga, kotak di samping saklar tukar → lampu r. keluarga lt2 (DED: di tembok KTU samping pintu) (h 1.40 m)

CATATAN

Posisi simbol dari gambar DED 1:100 yang dikalibrasi ke tembok model 3D; titik dinding digambar di muka tembok. Tinggi pasang (dari lantai jadi) mengikuti praktik umum/PUIL karena DED tidak mencantumkan tinggi. Angka +h.hh di samping simbol = tinggi yang menyimpang dari standar. Jalur kabel digambar skematis (ortogonal) mengikuti DED; kabel NYM dalam pipa PVC 5/8".

Rekomendasi: 2 stop kontak AC lt2 dan water heater KTU masing-masing ke grup MCB tersendiri (box ke-2 bisa di selasar lt2). Saklar tunggal = 1 kelompok lampu, ganda = 2 kelompok.