

Daftar kotak inbow (stop kontak & saklar Panasonic) dan titik lampu

Rumah Mbak Alfi · revisi 09-10-2026 · 1 kotak = 1 stop kontak / 1 saklar / 2 saklar · ID sama dengan label di model 3D (tekan E) dan angka di denah listrik 2D. Posisi x dari batas kavling kiri, z dari batas belakang (rumah x 3–10, z 3,5–13,5); h = tinggi as kotak dari lantai. Merah = tambahan / perubahan dari DED.

Lantai 1 — 32 kotak (23 stop kontak, 3 × 1 saklar, 5 × 2 saklar)

ID	Ruang	Isi kotak	h (m)	x, z (m)	Tembok	Keterangan
1-01	Teras belakang	1 stop kontak	1.20	9.88, 2.62	kanan	teras belakang: mesin cuci (di atas mesin, h 1,2)
1-02	Teras belakang	1 stop kontak	1.20	9.88, 3.27	kanan	REVISI: teras belakang: pompa pendorong (di atas pompa, h 1,2; DED: z 2.77 → digeser 50 cm)
1-03	Dapur	1 stop kontak	1.15	3.78, 3.56	belakang	BARU: dapur, tembok belakang di pojok kiri atas meja (rice cooker/microwave), jauh dari sink
1-04	Dapur	1 stop kontak	1.15	4.00, 3.56	belakang	BARU: dapur, tembok belakang di pojok kiri atas meja
1-05	Dapur	1 stop kontak	0.40	6.10, 3.58	belakang	dapur, tembok belakang (kulkas)
1-06	Dapur	1 stop kontak	0.40	6.30, 3.58	belakang	dapur, tembok belakang (kulkas)
1-07	Dapur	1 stop kontak	1.15	3.07, 5.25	kiri	dapur, di atas meja dapur, kanan jendela (gambar: z 5.47/5.69 menumpuk kusen jendela z 5.6–6.6 → digeser 22 cm)
1-08	Dapur	1 stop kontak	1.15	3.07, 5.47	kiri	dapur, di atas meja dapur
1-09	R. makan	1 stop kontak	0.40	5.56, 6.94	depan	ruang makan, tembok toilet
1-10	R. makan	1 stop kontak	0.40	5.77, 6.94	depan	ruang makan, tembok toilet
1-11	R. makan	2 saklar	1.40	6.30, 6.94	depan	ruang makan, tembok toilet → lampu dapur, r. makan, lorong
1-12	Pintu belakang (r. makan)	2 saklar	1.40	7.70, 3.56	belakang	REVISI: saklar ganda di kanan pintu belakang → lampu teras belakang + area jemur (DED: ganda; kotak Panasonic 2 saklar)
1-13	Pintu belakang (r. makan)	1 saklar tukar	1.40	7.80, 3.56	belakang	BARU: saklar tukar (two-way) lampu tangga/void, kotak kedua di kanan saklar ganda pintu belakang
1-14	Lemari bawah tangga	1 stop kontak (NVR/router)	0.40	9.88, 8.35	kanan	BARU: stop kontak NVR 4 ch PoE, di dalam lemari bawah tangga (bagian tinggi dekat r. keluarga)
1-15	Lemari bawah tangga	1 stop kontak (NVR/router)	0.40	9.88, 8.45	kanan	BARU: stop kontak router/switch, kotak kedua di samping stop kontak NVR
1-16	Toilet	1 stop kontak water heater (IP44)	1.82	4.45, 7.09	belakang	BARU: stop kontak water heater toilet lt1 (IP44), tembok sisi r. makan, kanan unit; 1,9 m di atas lantai toilet (–0,03)
1-17	Lorong	1 saklar	1.40	5.42, 8.44	depan	lorong depan toilet → lampu toilet
1-18	KT1	1 stop kontak	0.40	4.99, 8.56	belakang	KT1, tembok belakang (kiri pintu)
1-19	KT1	1 saklar	1.40	5.42, 8.56	belakang	KT1, kiri pintu → lampu KT1
1-20	KT1	1 stop kontak AC	2.40	3.06, 8.75	kiri	BARU: stop kontak AC KT1, tembok kiri mepet pojok tembok belakang (17 cm), di kiri unit indoor yang di atas jendela
1-21	KT1	1 stop kontak	0.40	3.06, 10.22	kiri	KT1, tembok kiri
1-22	R. keluarga	1 stop kontak	0.40	9.87, 9.20	kanan	REVISI: R. keluarga, tembok kanan dekat lemari bawah tangga, di balik pohon pot (DED: z 11.19)
1-23	R. keluarga	1 stop kontak	0.78	6.68, 10.30	kiri	BARU: dinding TV, di bawah TV di atas konsol, kotak 1 dari 4 (TV)
1-24	R. keluarga	1 stop kontak	0.78	6.68, 10.52	kiri	BARU: dinding TV, kotak 2 dari 4 (set-top box / Android TV box)
1-25	R. keluarga	1 stop kontak	0.78	6.68, 10.74	kiri	BARU: dinding TV, kotak 3 dari 4 (soundbar)
1-26	R. keluarga	1 stop kontak	0.78	6.68, 10.96	kiri	BARU: dinding TV, kotak 4 dari 4 (konsol game / router)
1-27	R. keluarga	1 stop kontak antena TV	0.78	6.68, 11.18	kiri	BARU: stop kontak antena TV (coax) di bawah TV, kotak ke-5 di kanan 4 stop kontak
1-28	R. keluarga	2 saklar	1.40	6.68, 11.69	kiri	R. keluarga, di muka panel TV → lampu r. keluarga
1-29	R. keluarga	2 saklar	1.40	6.66, 12.02	kiri	R. keluarga, samping pintu utama → lampu teras & carport
1-30	R. keluarga	1 stop kontak	0.35	9.87, 12.30	kanan	REVISI: R. keluarga, tembok kanan depan, di bawah meja samping melayang (bawah meja 0.41) (DED: z 10.72 di belakang sofa → digeser supaya sofa bisa mepet)

ID	Ruang	Isi kotak	h (m)	x, z (m)	Tembok	Keterangan
1-31	R. keluarga	1 stop kontak	0.35	9.87, 12.52	kanan	REVISI: R. keluarga, tembok kanan depan, di balik meja samping (DED: z 10.94)
1-32	Selasar samping (luar)	2 saklar	1.40	2.94, 10.22	kanan	teras samping (luar) → lampu taman/pagar

Lantai 2 — 23 kotak (14 stop kontak, 4 × 1 saklar, 4 × 2 saklar)

ID	Ruang	Isi kotak	h (m)	x, z (m)	Tembok	Keterangan
2-01	KT2	1 stop kontak	0.40	3.06, 5.33	kiri	KT2, tembok kiri
2-02	KT2	1 stop kontak AC	2.40	3.06, 5.45	kiri	BARU: stop kontak AC KT2, tembok kiri di kiri unit indoor yang di atas jendela
2-03	KT2	1 stop kontak	0.40	6.43, 5.45	kanan	KT2, tembok kanan
2-04	KT2	1 saklar	1.40	6.43, 5.88	kanan	KT2, samping pintu → lampu KT2 (simbol DED: tunggal, 1 kelompok lampu)
2-05	Selasar	1 saklar	1.40	7.73, 3.56	belakang	selasar, kanan pintu balkon belakang → lampu balkon
2-06	Selasar	1 stop kontak	0.40	6.56, 5.45	kiri	selasar, tembok KT2
2-07	Selasar	2 saklar	1.40	6.56, 8.15	kiri	REVISI: selasar, samping pintu toilet kanan → 1 tuts lampu toilet kanan + 1 tuts 3 lampu selasar (2 selasar + 1 depan pintu KTU); menggantikan saklar selasar DED di z 5,88
2-08	Toilet kiri (KTU)	1 stop kontak water heater (IP44)	1.90	4.50, 7.09	belakang	BARU: stop kontak water heater toilet lt2 kiri (di dalam KTU, IP44), tembok sisi KT2, kanan unit, 1,1 m dari kepala shower
2-09	KT utama	2 saklar	1.40	4.07, 8.56	belakang	KTU, kanan pintu toilet → lampu toilet kiri + lampu balkon samping kiri (simbol DED: ganda, 2 kelompok)
2-10	KT utama	1 saklar	1.40	6.43, 9.57	kanan	KTU, samping pintu → lampu KTU
2-11	KT utama	1 stop kontak	0.40	6.43, 10.01	kanan	KTU, tembok kanan (meja rias)
2-12	KT utama	1 stop kontak AC	2.40	3.06, 10.30	kiri	BARU: stop kontak AC KTU, tembok kiri di kanan unit indoor yang di atas pintu geser balkon
2-13	KT utama	1 stop kontak	0.40	3.06, 10.75	kiri	KTU, tembok kiri
2-14	R. keluarga lt2	1 saklar tukar	1.40	9.88, 9.45	kanan	BARU: saklar tukar (two-way) lampu tangga/void di tembok luar, tepat setelah anak tangga teratas — pasangan saklar triple lt1 di pintu belakang
2-15	R. keluarga lt2	2 saklar	1.40	9.88, 9.55	kanan	REVISI: R. keluarga lt2, tembok luar setelah tangga, kotak di samping saklar tukar → lampu r. keluarga lt2 (DED: di tembok KTU samping pintu)
2-16	R. keluarga lt2	1 stop kontak	0.40	6.56, 9.72	kiri	BARU: R. keluarga lt2, tembok KTU (seberang), strip bebas di kanan pintu KTU
2-17	R. keluarga lt2	1 stop kontak	1.05	6.56, 10.90	kiri	BARU: R. keluarga lt2, tembok KTU di atas sideboard (top 0.80)
2-18	R. keluarga lt2	1 stop kontak	1.05	6.56, 11.12	kiri	BARU: R. keluarga lt2, tembok KTU di atas sideboard
2-19	R. keluarga lt2	2 saklar	1.40	6.56, 12.02	kiri	R. keluarga lt2, samping pintu balkon → lampu balkon depan + sorot
2-20	R. keluarga lt2	1 stop kontak antena TV	0.40	9.88, 12.19	kanan	BARU: stop kontak antena TV (coax) di bawah meja kerja, kiri 3 stop kontak meja
2-21	R. keluarga lt2	1 stop kontak	0.40	9.88, 12.41	kanan	R. keluarga lt2, tembok kanan depan
2-22	R. keluarga lt2	1 stop kontak	0.40	9.88, 12.63	kanan	R. keluarga lt2, tembok kanan depan

ID	Ruang	Isi kotak	h (m)	x, z (m)	Tembok	Keterangan
2-23	R. keluarga lt2	1 stop kontak	0.40	9.88, 12.85	kanan	R. keluarga lt2, tembok kanan depan

Rekap belanja kotak

Kotak 1 stop kontak (termasuk 3 AC, 2 water heater IP44, 2 NVR)	37
Kotak 1 saklar (termasuk 2 saklar tukar)	7
Kotak 2 saklar	9
Kotak stop kontak antena TV (coax; 1 antena di atap + splitter 2 way)	2
Total kotak / inbow doos	55

Stop kontak water heater (1-16, 2-08) perlu varian tertutup (IP44). Ukuran pelat 90 mm = asumsi dari inbow doos 86 mm; cocokkan dengan kemasan produk. Dibuat otomatis dari data model 3D (scripts/denah-listrik.mjs).

Daftar titik lampu — revisi 09-10-2026

DED menentukan jumlah & titik (dasar RAB); armatur SKP $\leq 0,5$ m dari titik DED → posisi SKP dipakai; lampu yang hanya di SKP dipakai bila fungsional. h = tinggi pasang dari lantai ybs (lampu plafon = tinggi plafon). ID sama dengan label kuning di 3D (tekan E) dan di denah.

Lantai 1 — 34 titik

ID	Ruang	Jenis	Daya	h (m)	x, z (m)	Sumber	Keterangan / evaluasi
L1-01	Taman samping	Lampu dinding outdoor (up-down)	5 W	1.40 (dinding, hadap kanan)	0.12, 0.30	baru	taman samping, tembok batas kiri pojok belakang, di belakang pintu samping (DED; belum ada di model 3D sebelumnya). Kabel & saklar ikut lampu r. jemur (garis DED menyambung lewat pagar belakang)
L1-02	Taman samping	Lampu dinding outdoor (up-down)	5 W	1.40 (dinding, hadap kanan)	0.12, 3.70	baru	taman samping, tembok batas kiri (DED; belum ada di model 3D sebelumnya)
L1-03	Taman samping	Lampu dinding outdoor (up-down)	5 W	1.40 (dinding, hadap kanan)	0.12, 6.00	baru	taman samping, tembok batas kiri (DED; belum ada di model 3D sebelumnya)
L1-04	Taman samping	Lampu dinding outdoor (up-down)	5 W	1.40 (dinding, hadap kanan)	0.12, 15.00	baru	samping carport, tembok batas kiri (DED; belum ada di model 3D sebelumnya)
L1-05	Taman samping (dek)	Lampu dinding outdoor (up-down)	5 W	1.40 (dinding, hadap kanan)	0.24, 9.98	DED, posisi SKP	taman samping, panel dinding dek (posisi SKP; DED z 8,57 di ujung panel)
L1-06	Taman samping (dek)	Downlight tanam	9 W	3.15 (plafon)	2.18, 10.21	DED, posisi SKP	bawah balkon samping (dek taman), plafon kayu (posisi SKP). DED hanya 1 titik di 1,55 / 10,97 = di tepi luar balkon → diganti 2 titik SKP di tengah plafon
L1-07	Taman samping (dek)	Downlight tanam	9 W	3.15 (plafon)	2.18, 11.83	SKP (tidak ada di DED)	bawah balkon samping (dek taman), titik kedua (posisi SKP; +1 dari DED)
L1-08	Taman samping (dek)	Lampu dinding outdoor (up-down)	5 W	1.40 (dinding, hadap kanan)	0.24, 12.03	DED, posisi SKP	taman samping, panel dinding dek (posisi SKP; DED z 13,43 di ujung panel)
L1-09	Teras belakang	Downlight tanam	9 W	3.45 (plafon)	8.19, 2.72	DED, posisi SKP	teras belakang (DED 8,30 / 2,74; armatur SKP 11 cm dari titik DED → dipakai posisi SKP)
L1-10	R. jemur	Lampu dinding outdoor (up-down)	5 W	1.40 (dinding, hadap depan)	3.84, 0.13	DED, diubah	r. jemur, muka dalam pagar belakang (DED). Tinggi 1,75 → 1,40 m, sejajar lampu taman
L1-11	Dapur	Downlight tanam	9 W	3.60 (plafon)	4.76, 5.24	DED	dapur
L1-12	R. makan	Titik lampu gantung	—	3.60 (plafon)	5.08, 6.54	baru	lampu gantung di atas meja makan (furnitur; tidak ada di DED → titik baru). Bawah bola lampu 1,56 m dari lantai = 0,80 m di atas meja (dulu 1,42 m di atas meja — terlalu tinggi; standar 0,75–0,90 m)
L1-13	R. makan (sisi tangga)	Downlight tanam	5 W	3.60 (plafon)	7.09, 5.24	DED	r. makan sisi tangga
L1-14	Toilet	Downlight tanam	5 W	3.60 (plafon)	3.87, 7.74	DED	toilet
L1-15	Lorong	Downlight tanam	5 W	3.60 (plafon)	7.09, 7.74	DED	lorong
L1-16	KT1	Downlight tanam	9 W	3.60 (plafon)	4.76, 10.22	DED	KT1
L1-17	R. keluarga	Downlight tanam	5 W	3.60 (plafon)	7.09, 8.98	DED	r. keluarga

ID	Ruang	Jenis	Daya	h (m)	x, z (m)	Sumber	Keterangan / evaluasi
L1-18	R. keluarga	Downlight tanam	5 W	3.35 (plafon)	9.42, 8.98	DED	r. keluarga, plafon turun dekat tangga
L1-19	R. keluarga	Downlight tanam	5 W	3.60 (plafon)	7.09, 10.94	DED	r. keluarga
L1-20	R. keluarga	Downlight tanam	5 W	3.60 (plafon)	9.44, 10.94	DED	r. keluarga
L1-21	R. keluarga	Titik lampu gantung	—	3.60 (plafon)	8.20, 11.20	DED, diubah	r. keluarga: lampu gantung cincin di atas meja kopi, menggantikan titik 9 W DED (8,26 / 10,94; berimpit 27 cm). Cincin terbawah 2,20 m dari lantai (dulu kanopinya melayang 45 cm di bawah plafon)
L1-22	R. keluarga	Downlight tanam	5 W	3.60 (plafon)	7.09, 12.94	DED	r. keluarga
L1-23	R. keluarga	Downlight tanam	5 W	3.60 (plafon)	9.44, 12.94	DED	r. keluarga
L1-24	Teras depan	Downlight tanam	9 W	3.15 (plafon)	4.69, 12.83	DED, posisi SKP	teras depan, plafon bawah dak lt2 (DED 4,75 / 12,72; posisi SKP)
L1-25	Fasad depan	Lampu dinding outdoor (up-down)	5 W	2.00 (dinding, hadap depan)	6.99, 13.56	DED, diubah	fasad lt1 di samping pintu utama (DED). Tinggi 2,30 → 2,00 m
L1-26	Fasad depan	Lampu dinding outdoor (up-down)	5 W	2.00 (dinding, hadap depan)	3.10, 13.59	DED, diubah	fasad lt1 kiri, kolom putih (DED). Tinggi 2,30 → 2,00 m: sejajar atas kusen pintu, standar lampu dinding fasad 1,8–2,1 m
L1-27	Carport	Downlight tempel (outbow)	9 W	2.82 (atap, bawah lampu 2.68)	4.77, 15.00	DED, diubah	carport (DED), downlight tempel di bawah atap spandek (tidak bisa ditanam); bawah armatur ±2,68 m dari lantai
L1-28	Carport	Downlight tempel (outbow)	9 W	2.85 (atap, bawah lampu 2.71)	8.30, 15.00	DED, diubah	carport (DED), downlight tempel
L1-29	Carport	Downlight tempel (outbow)	9 W	2.82 (atap, bawah lampu 2.68)	4.77, 18.00	DED, diubah	carport sisi pagar (DED), downlight tempel
L1-30	Carport	Downlight tempel (outbow)	9 W	2.85 (atap, bawah lampu 2.71)	8.30, 18.00	DED, diubah	carport sisi pagar (DED), downlight tempel
L1-31	Luar pagar (sisi jalan)	Lampu sorot taman (spike, sorot ke atas)	5 W	kepala lampu di bak tanaman (sorot ke atas)	3.60, 19.17	DED, posisi SKP	sisi jalan, lampu sorot taman (spike) di bak tanaman di antara dua semak, menyorot dinding bertekstur ke atas (render hal. 4 & 6; armatur SKP). Sebelumnya salah kucatat sebagai lampu dinding. IP65
L1-32	Luar pagar (sisi jalan)	Downlight tanam	5 W	2,00 dari trotoar (plafon kanopi pintu pagar)	2.22, 19.23	SKP (tidak ada di DED)	sisi jalan, di plafon kanopi pintu pagar pejalan kaki (hanya di SKP; dipertahankan: menerangi pintu pagar, bel & nomor rumah). 2,0 m dari trotoar
L1-33	R. jemur	Lampu sorot taman (spike, sorot ke atas)	5 W	kepala lampu 0,17 di atas kerikil (sorot ke atas)	6.45, 1.50	SKP (tidak ada di DED)	lampu sorot taman bertiang pendek (spike) di bak kerikil kaki dinding roster, menyorot roster ke atas (hanya di SKP; sempat salah kuanggap penutup floor drain). Dipertahankan sebagai aksesoris roster. Pakai tipe IP65, kabel outdoor dari grup lampu jemur lewat kolom roster lalu di bawah kerikil
L1-34	Carport	Lampu sorot tanam lantai (sorot ke atas)	5 W	rata paving, 15 cm dari tembok (sorot ke atas)	9.72, 18.70	baru	carport sisi gerbang, lampu sorot tanam lantai di kaki tembok batas kanan 0,75 m dari gerbang, menyorot tembok ke atas: pasangan lampu sorot dinding tekstur di sisi pintu pagar (tidak ada di DED/SKP; tambahan 09-10-2026). Wajib tipe tanam IP67 tahan dilindas mobil (drive-over). Grup lampu carport

Lantai 2 — 20 titik

ID	Ruang	Jenis	Daya	h (m)	x, z (m)	Sumber	Keterangan / evaluasi
L2-01	Balkon belakang	Downlight tanam	9 W	2.40 (plafon)	8.19, 2.72	DED, posisi SKP	balkon belakang (DED 8,30 / 2,74; posisi SKP)
L2-02	KT2	Downlight tanam	9 W	3.40 (plafon)	4.76, 5.24	DED	KT2
L2-03	Selasar	Downlight tanam	5 W	3.40 (plafon)	7.09, 4.99	DED	selasar
L2-04	Selasar	Downlight tanam	5 W	3.40 (plafon)	7.09, 6.98	DED	selasar
L2-05	Void tangga	Downlight tanam	9 W	3.05 (plafon)	9.42, 4.99	DED	void tangga
L2-06	Void tangga	Downlight tanam	9 W	3.05 (plafon)	9.42, 6.98	DED	void tangga
L2-07	Toilet kiri (KTU)	Downlight tanam	5 W	3.40 (plafon)	3.87, 7.74	DED	toilet kiri (KTU)
L2-08	Toilet kanan	Downlight tanam	5 W	3.40 (plafon)	5.66, 7.74	DED	toilet kanan
L2-09	KT utama	Downlight tanam	9 W	3.40 (plafon)	4.76, 10.22	DED	KT utama
L2-10	R. keluarga lt2	Downlight tanam	5 W	3.40 (plafon)	7.09, 8.98	DED	r. keluarga lt2 (depan pintu KTU)
L2-11	R. keluarga lt2	Downlight tanam	5 W	3.05 (plafon)	9.42, 8.98	DED	r. keluarga lt2
L2-12	R. keluarga lt2	Downlight tanam	5 W	3.40 (plafon)	7.09, 10.94	DED	r. keluarga lt2
L2-13	R. keluarga lt2	Downlight tanam	9 W	3.40 (plafon)	8.26, 10.94	DED	r. keluarga lt2 tengah
L2-14	R. keluarga lt2	Downlight tanam	5 W	3.05 (plafon)	9.44, 10.94	DED	r. keluarga lt2
L2-15	R. keluarga lt2	Downlight tanam	5 W	3.40 (plafon)	7.09, 12.94	DED	r. keluarga lt2
L2-16	R. keluarga lt2	Downlight tanam	5 W	3.05 (plafon)	9.44, 12.94	DED	r. keluarga lt2
L2-17	Balkon depan	Downlight tanam	9 W	2.40 (plafon)	2.14, 12.83	DED, posisi SKP	balkon depan, pojok kiri (DED 2,24 / 12,73; posisi SKP)
L2-18	Balkon depan	Downlight tanam	9 W	2.40 (plafon)	5.01, 12.83	DED, posisi SKP	balkon depan (DED 4,74 / 12,73; posisi SKP 27 cm dari DED)
L2-19	Fasad lt2	Lampu dinding outdoor (up-down)	5 W	1.15 (dinding, hadap depan)	6.07, 13.95	DED = SKP	fasad lt2 di panel kisi kayu (posisi SKP; simbol DED di x 6,99), 1,15 m di atas lantai lt2: lampu aksent fasad
L2-20	Balkon samping	Downlight tanam	9 W	2.40 (plafon)	2.14, 9.58	DED, posisi SKP	balkon samping (DED 2,24 / 9,48; posisi SKP)

Rekap titik lampu


Downlight tanam 9 W	15
Downlight tanam 5 W	20
Downlight tempel (outbow) 9 W — carport	4
Lampu dinding outdoor 5 W	10
Lampu sorot taman (spike) 5 W, sorot ke atas	2
Lampu sorot tanam lantai 5 W IP67, sorot ke atas	1
Titik lampu gantung (armatur furnitur)	2
Total titik lampu	54
— di antaranya armatur sudah ada di model SKP	14
— diubah dari DED (posisi / jenis / tinggi)	18
— baru (tidak ada di DED)	9

Lampu di model SKP yang tidak dipakai (disembunyikan di 3D)

x, y, z (m)	Alasan
3.86, 2.70, 15.86	carport, baris tengah (SKP 5 lampu, tanpa lampu di sisi pagar) → diganti grid 2x2 DED

x, y, z (m)	Alasan
6.26, 2.70, 15.86	carport, baris tengah
8.66, 2.70, 15.86	carport, baris tengah
7.71, 2.70, 13.68	carport, depan kaca r. keluarga
8.67, 2.70, 13.68	carport, depan kaca r. keluarga
2.69, 6.04, 6.16	luifel jendela KT2 sisi luar, 6 m di atas selasar samping (dekoratif)
2.14, 6.24, 11.21	balkon samping, titik tambahan di antara 2 titik DED (jarak DED 3,25 m sudah cukup)
3.57, 6.24, 12.83	balkon depan, titik tambahan
8.22, 6.24, 13.80	atas bak tanaman di depan kaca r. keluarga lt2 (dekoratif)

Catatan tinggi: plafon dalam rumah tinggi (3,60 m lt1, 3,40 m lt2) — downlight 5 W (± 450 lm) di plafon setinggi itu terasa redup untuk ruang keluarga/makan; pertimbangkan 7–9 W untuk titik 5 W di ruang keluarga. Lampu taman dinding 1,40 m dari lantai teras = 1,45–1,80 m dari tanah/dek (standar 1,5–1,8 m). Lampu dinding fasad 2,00 m (standar 1,8–2,1 m). Lampu gantung: cincin r. keluarga terbawah 2,20 m ($\geq 2,1$ m area lalu-lalang); lampu meja makan 0,80 m di atas meja (standar 0,75–0,90 m).

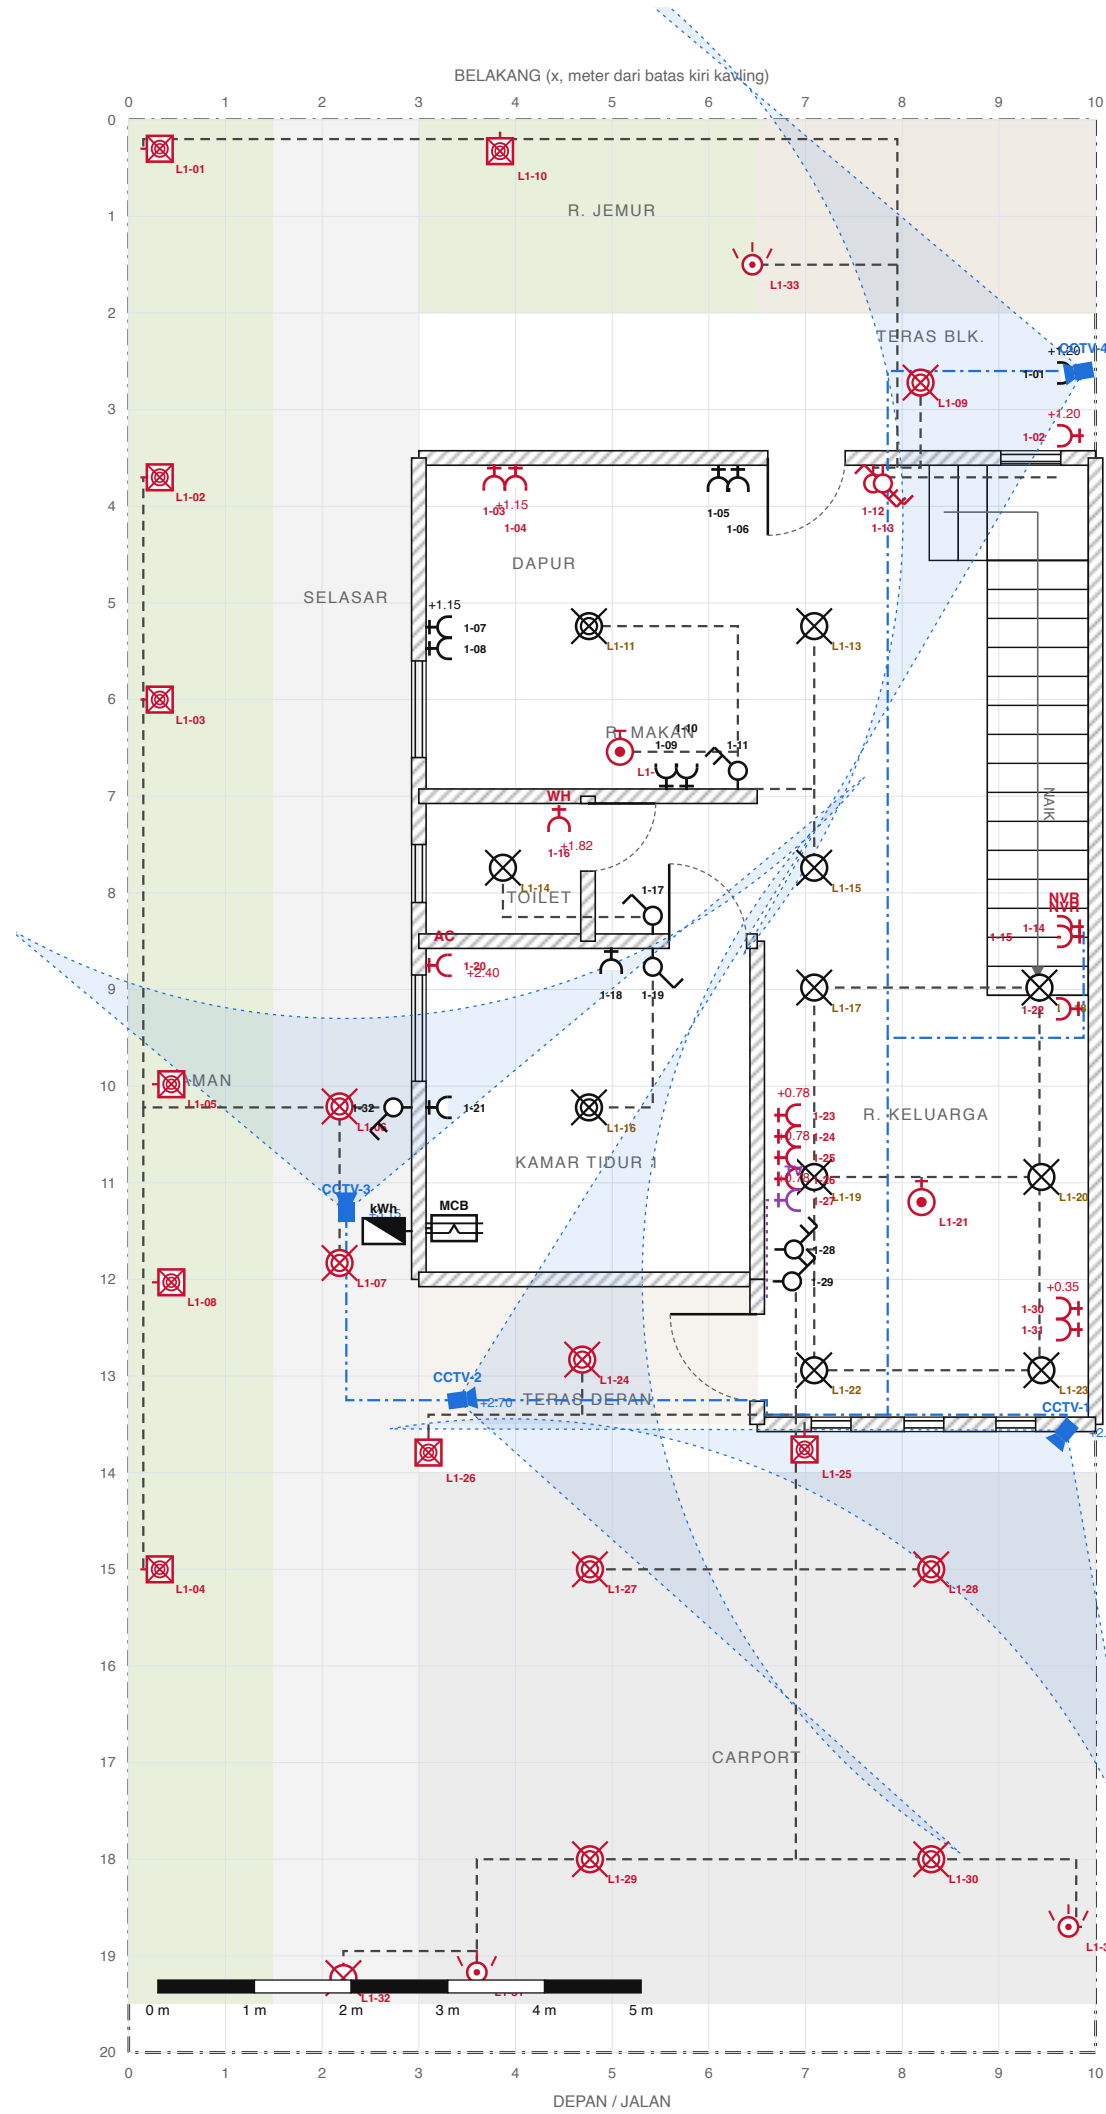

Dibuat otomatis dari data model 3D (scripts/denah-listrik.mjs) · 09-10-2026

DENAH INSTALASI LISTRIK

LANTAI 1 — REVISI 09-10-2026

Rumah Mbak Alfi · skala 1 : 100 pada A3 (1 m = 60 px) · dasar: DED lembar 26 (hal. 69)


SIMBOL	KETERANGAN	ADA	BARU
	Stop kontak 1 ph 10/16 A, h 40 cm (dapur 115, mesin cuci 120)	13	+8
	Stop kontak AC, h 240 cm (unit indoor di atas jendela)	0	+1
	Stop kontak water heater IP44, h 190 cm, grup sendiri	0	+1
	Stop kontak antenna TV (coax IEC), 1 antenna di atap + splitter 2 way	0	+1
	Saklar tunggal, h 140 cm	2	-
	Saklar ganda, h 140 cm	5	-
	Saklar tukar (two-way) lampu tangga, h 140 cm	0	+1
	Kotak inbow Panasonic (1 kotak = 1 stop kontak / 1 saklar / 2 saklar); angka = ID kotak (32 kotak, lihat daftar-kotak.md)		
	Lampu LED downlight 5 W	9	+1
	Lampu LED downlight 9 W (carport: model tempel/outbow)	9	+1
	Lampu sorot ke atas 5 W: taman/spike IP65 (roster jemur, dinding tekstur pagar) & tanam lantai IP67 (carport)	1	+2
	Titik lampu gantung (armatur dari furnitur)	1	+1
	Lampu LED dinding outdoor 5 W (taman: h 140 cm)	5	+4
	Angka L1-xx = ID titik lampu (34 titik, lihat Daftar Titik Lampu)		
	Box MCB 4 group x 10 A, h 175 cm	1	-
	kWh meter PLN 2200 VA (sisi luar), h 170 cm	1	-
	Jalur kabel NYM 2x2,5 mm² dalam pipa, di bawah dak/plafon		
	CCTV IP PoE 2 MP outdoor (kerucut = sudut pandang 100°, 7 m)	0	+4
	NVR 4 ch PoE + HDD di lemari bawah tangga (stop kontak ganda)	0	+2
	Kabel data CAT6 ke NVR, dalam pipa 3/4"		
	Kabel coax RG6 antenna (splitter di plafon r. keluarga lt2)		

REVISI 09-10-2026 (merah = tambahan / perubahan dari DED)

- Lampu (revisi 09-10-2026): 34 titik, 14 posisi/jenis/tinggi diubah, 9 baru → rincian & tinggi pasang di Daftar Titik Lampu (merah = berubah dari DED)
- teras belakang: pompaendorong (di atas pompa, h 1,2; DED: z 2.77 → digeser 50 cm) (h 1.20 m)
- R. keluarga, tembok belakang di pojok kiri atas meja (rice cooker/microwave), jauh dari sink (h 1.15 m)
- dapur, tembok belakang di pojok kiri atas meja (h 1.15 m)
- R. keluarga, tembok kanan depan, di bawah meja samping melayang (bawah meja 0.41) (DED: z 10.72 di belakang sofa → digeser supaya sofa bisa mepet) (h 0.35 m)
- R. keluarga, tembok kanan depan, di balik meja samping (DED: z 10.94) (h 0.35 m)
- R. keluarga, tembok kanan dekat lemari bawah tangga, di balik pohon pot (DED: z 11.19) (h 0.40 m)
- dinding TV: 4 stop kontak di bawah TV di atas konsol (TV, set-top box, soundbar, konsol/router) (h 0.78 m)
- stop kontak antenna TV (coax) di bawah TV, kotak ke-5 di kanan 4 stop kontak (h 0.78 m)
- stop kontak AC KT1, tembok kiri mepet pojok tembok belakang (17 cm), di kiri unit indoor yang di atas jendela (h 2.40 m)
- stop kontak water heater toilet lt1 (IP44), tembok sisi r. makan, kanan unit; 1,9 m di atas lantai toilet (-0.03) (h 1.82 m)
- CCTV-1 carport & gerbang: pojok kanan fasad di bawah tepi kanopi, menghadap gerbang (-40° ke kiri) sehingga mulut selasar kiri ikut terlihat, tunduk 15° (h 2.70 m)
- CCTV-2 teras depan & pintu utama: di plafon teras (bawah balkon) pojok kiri-depan, menghadap pintu utama (+x), tunduk 20° (h 2.70 m)
- CCTV-3 selasar samping kiri: di bawah balkon samping (tengah), menghadap ke belakang: selasar z 4-11 dalam 7 m, sambung dengan CCTV-4 yang menutup ujung belakang; mulut depan selasar ditangkap CCTV-1 (h 3.15 m)
- CCTV-4 belakang: tembok batas kanan di bawah balkon belakang, menghadap teras belakang, pintu belakang, area jemur & ujung belakang selasar (+10°), tunduk 17° (h 3.10 m)
- stop kontak NVR 4 ch PoE, di dalam lemari bawah tangga (bagian tinggi dekat r. keluarga) (h 0.40 m)
- stop kontak router/switch, kotak kedua di samping stop kontak NVR (h 0.40 m)
- saklar ganda di kanan pintu belakang → lampu teras belakang + area jemur (DED: ganda; kotak Panasonic 2 saklar) (h 1.40 m)
- saklar tukar (two-way) lampu tangga/void, kotak kedua di kanan saklar ganda pintu belakang (h 1.40 m)
- TV 65" diturunkan: bawah 0,80 m, tengah layar 1,22 m (mata duduk ±1,10 m)
- Stop kontak dapur kiri digeser 22 cm ke kanan jendela (jendela z 5,6-6,6)

CATATAN

Posisi simbol dari gambar DED 1:100 yang dikalibrasi ke tembok model 3D; titik dinding digambar di muka tembok. Tinggi pasang (dari lantai jadi) mengikuti praktik umum/PUIL karena DED tidak mencantumkan tinggi.
Angka +h.hh di samping simbol = tinggi yang menyimpang dari standar. Jalur kabel digambar skematis (ortogonal) mengikuti DED: kabel NYM dalam olca PVC 5/8".

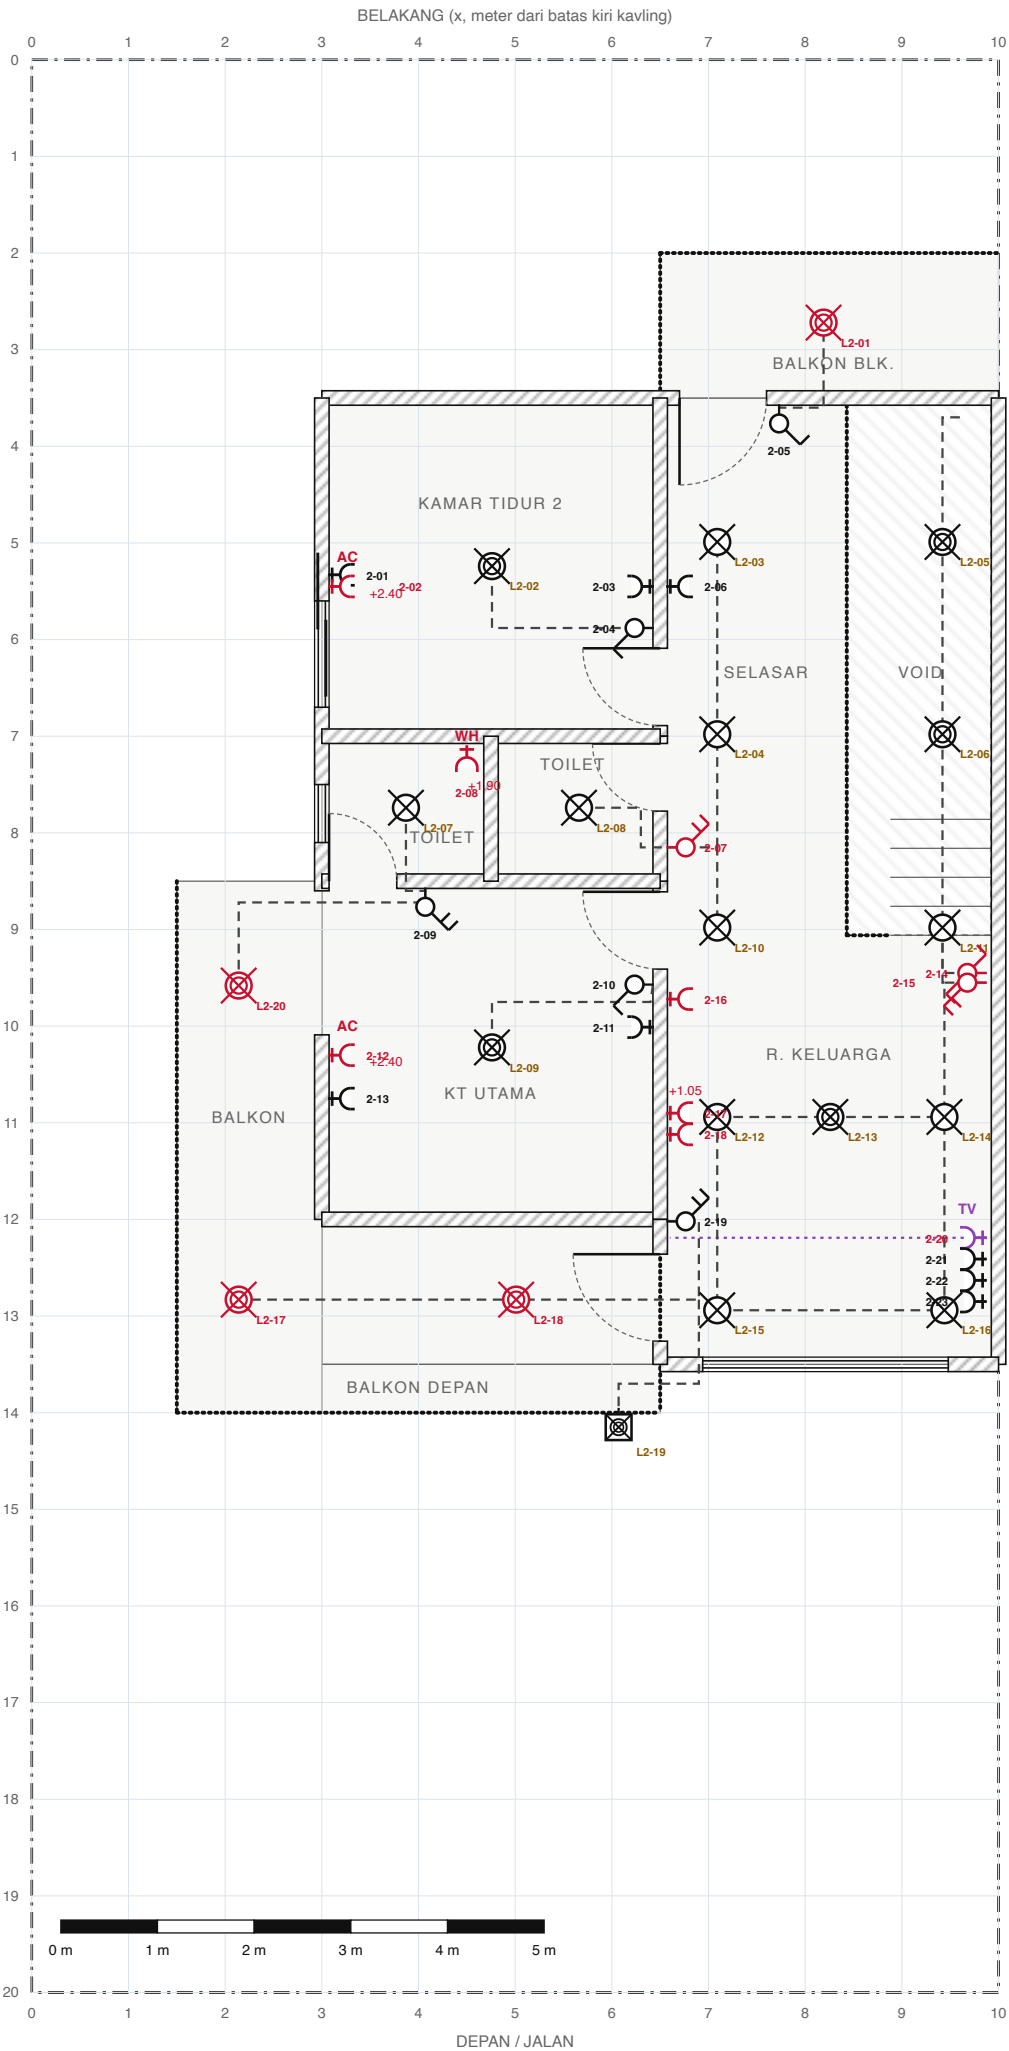

DENAH INSTALASI LISTRIK
LANTAI 2 — REVISI 09-10-2026

Rumah Mbak Alfi · skala 1 : 100 pada A3 (1 m = 60 px) · dasar: DED lembar 27 (hal. 70)

SIMBOL	KETERANGAN	ADA	BARU
	Stop kontak 1 ph 10/16 A, h 40 cm (dapur 115, mesin cuci 120)	8	+3
	Stop kontak AC, h 240 cm (unit indoor di atas jendela)	0	+2
	Stop kontak water heater IP44, h 190 cm, grup sendiri	0	+1
	Stop kontak antenna TV (coax IEC), 1 antenna di atap + splitter 2 way	0	+1
	Saklar tunggal, h 140 cm	3	-
	Saklar ganda, h 140 cm	4	-
	Saklar tukar (two-way) lampu tangga, h 140 cm	0	+1
	Kotak inbow Panasonic (1 kotak = 1 stop kontak / 1 saklar / 2 saklar); angka = ID kotak (23 kotak, lihat daftar-kotak.md)		
	Lampu LED downlight 5 W	10	-
	Lampu LED downlight 9 W	9	-
	Titik lampu gantung (armatur dari furnitur)	0	-
	Lampu LED dinding outdoor 5 W (taman: h 140 cm)	1	-
	Angka L2-xx = ID titik lampu (20 titik, lihat Daftar Titik Lampu)		
	Box MCB 4 group x 10 A, h 175 cm	0	-
	kWh meter PLN 2200 VA (sisi luar), h 170 cm	0	-
	Jalur kabel NYM 2x2,5 mm² dalam pipa, di bawah dak/plafon		
	Kabel coax RG6 antenna (splitter di plafon r. keluarga lt2)		

REVISI 09-10-2026 (merah = tambahan / perubahan dari DED)

- Lampu (revisi 09-10-2026): 20 titik, 4 posisi/jenis/tinggi diubah, 0 baru — rincian & tinggi pasang di Daftar Titik Lampu (merah = berubah dari DED)
- stop kontak antenna TV (coax) di bawah meja kerja, kiri 3 stop kontak meja (h 0.40 m)
- stop kontak AC KT2, tembok kiri di kiri unit indoor yang di atas jendela (h 2.40 m)
- stop kontak AC KTU, tembok kiri di kanan unit indoor yang di atas pintu geser balkon (h 2.40 m)
- R. keluarga lt2, tembok KTU (seberang), strip bebas di kanan pintu KTU (h 0.40 m)
- R. keluarga lt2, tembok KTU di atas sideboard (top 0.80) (h 1.05 m)
- R. keluarga lt2, tembok KTU di atas sideboard (h 1.05 m)
- stop kontak water heater toilet lt2 kiri (di dalam KTU, IP44), tembok sisi KT2, kanan unit, 1,1 m dari kepala shower (h 1.90 m)
- saklar tukar (two-way) lampu tangga/void di tembok luar, tepat setelah anak tangga teratas — pasangan saklar triple lt1 di pintu belakang (h 1.40 m)
- selasar, samping pintu toilet kanan → 1 tuts lampu toilet kanan + 1 tuts 3 lampu selasar (2 selasar + 1 depan pintu KTU); menggantikan saklar selasar DED di z 5,88 (h 1.40 m)
- R. keluarga lt2, tembok luar setelah tangga, kotak di samping saklar tukar → lampu r. keluarga lt2 (DED: di tembok KTU samping pintu) (h 1.40 m)

CATATAN

Posisi simbol dari gambar DED 1:100 yang dikalibrasi ke tembok model 3D; titik dinding digambar di muka tembok. Tinggi pasang (dari lantai jadi) mengikuti praktik umum/PUIL karena DED tidak mencantumkan tinggi.
Angka +h.hh di samping simbol = tinggi yang menyimpang dari standar. Jalur kabel digambar skematis (ortogonal) mengikuti DED; kabel NYM dalam pipa PVC 5/8".
Rekomendasi: 2 stop kontak AC lt2 dan water heater KTU masing-masing ke grup MCB tersendiri (box ke-2 bisa di selasar lt2). Saklar tunggal = 1 kelompok lampu, ganda = 2 kelompok.